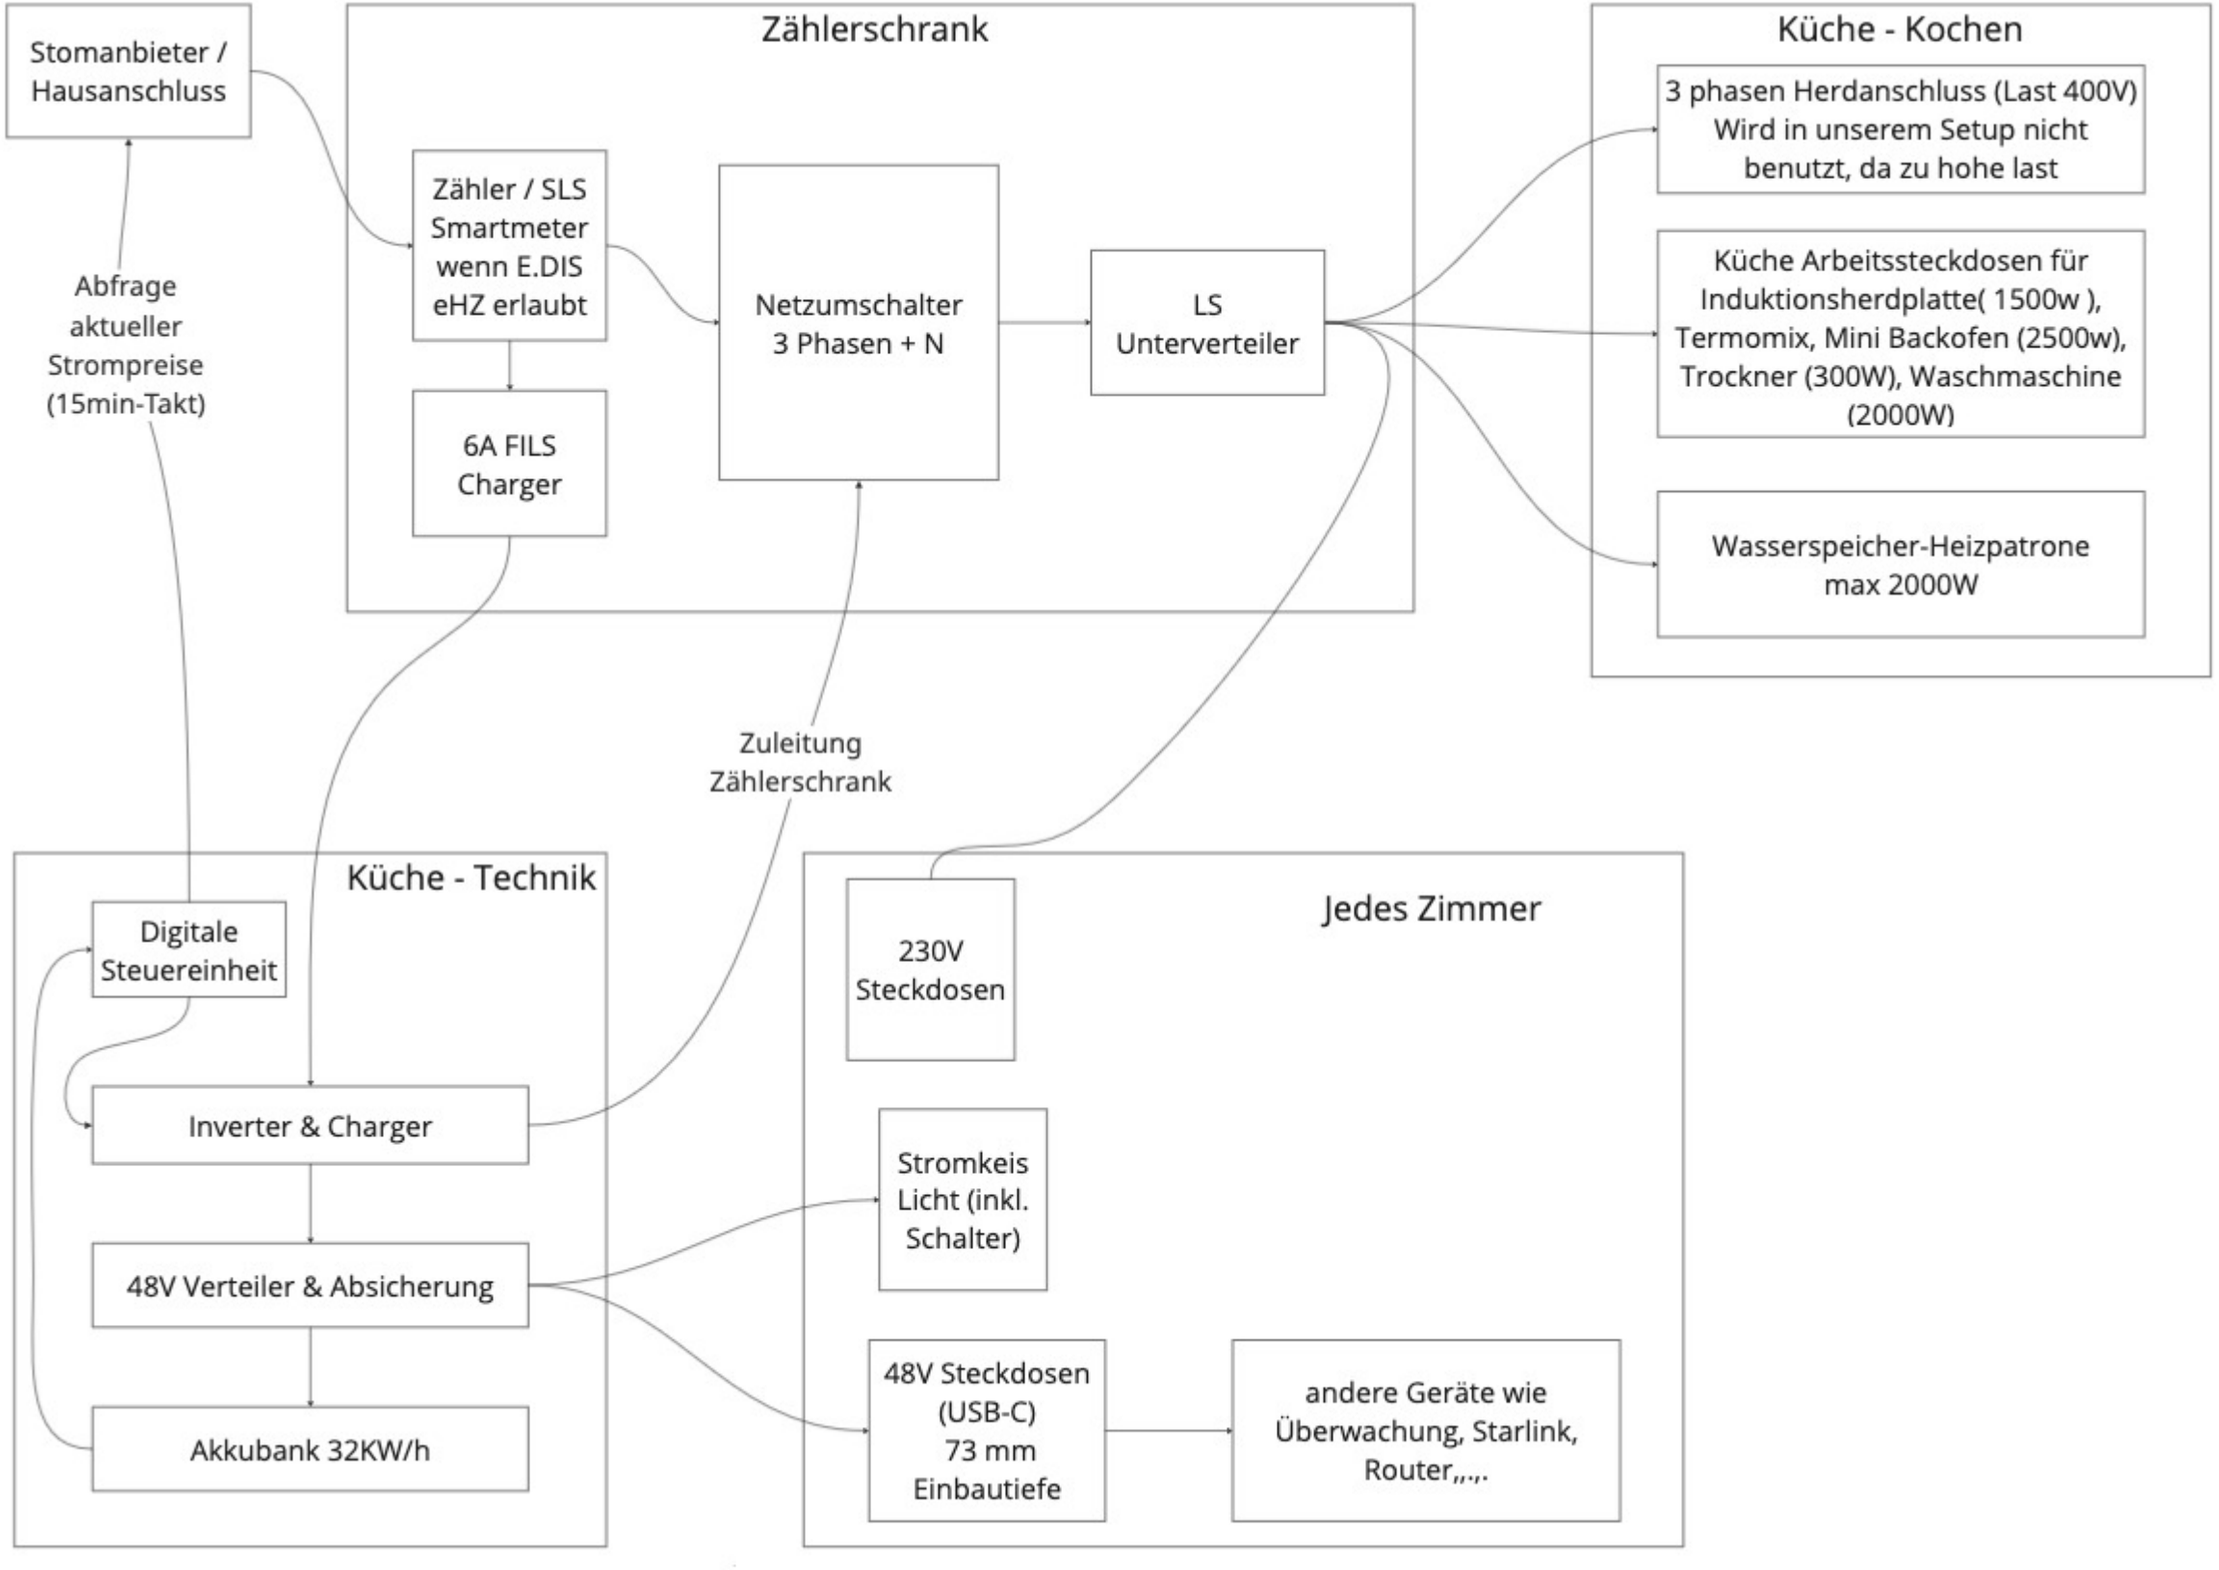
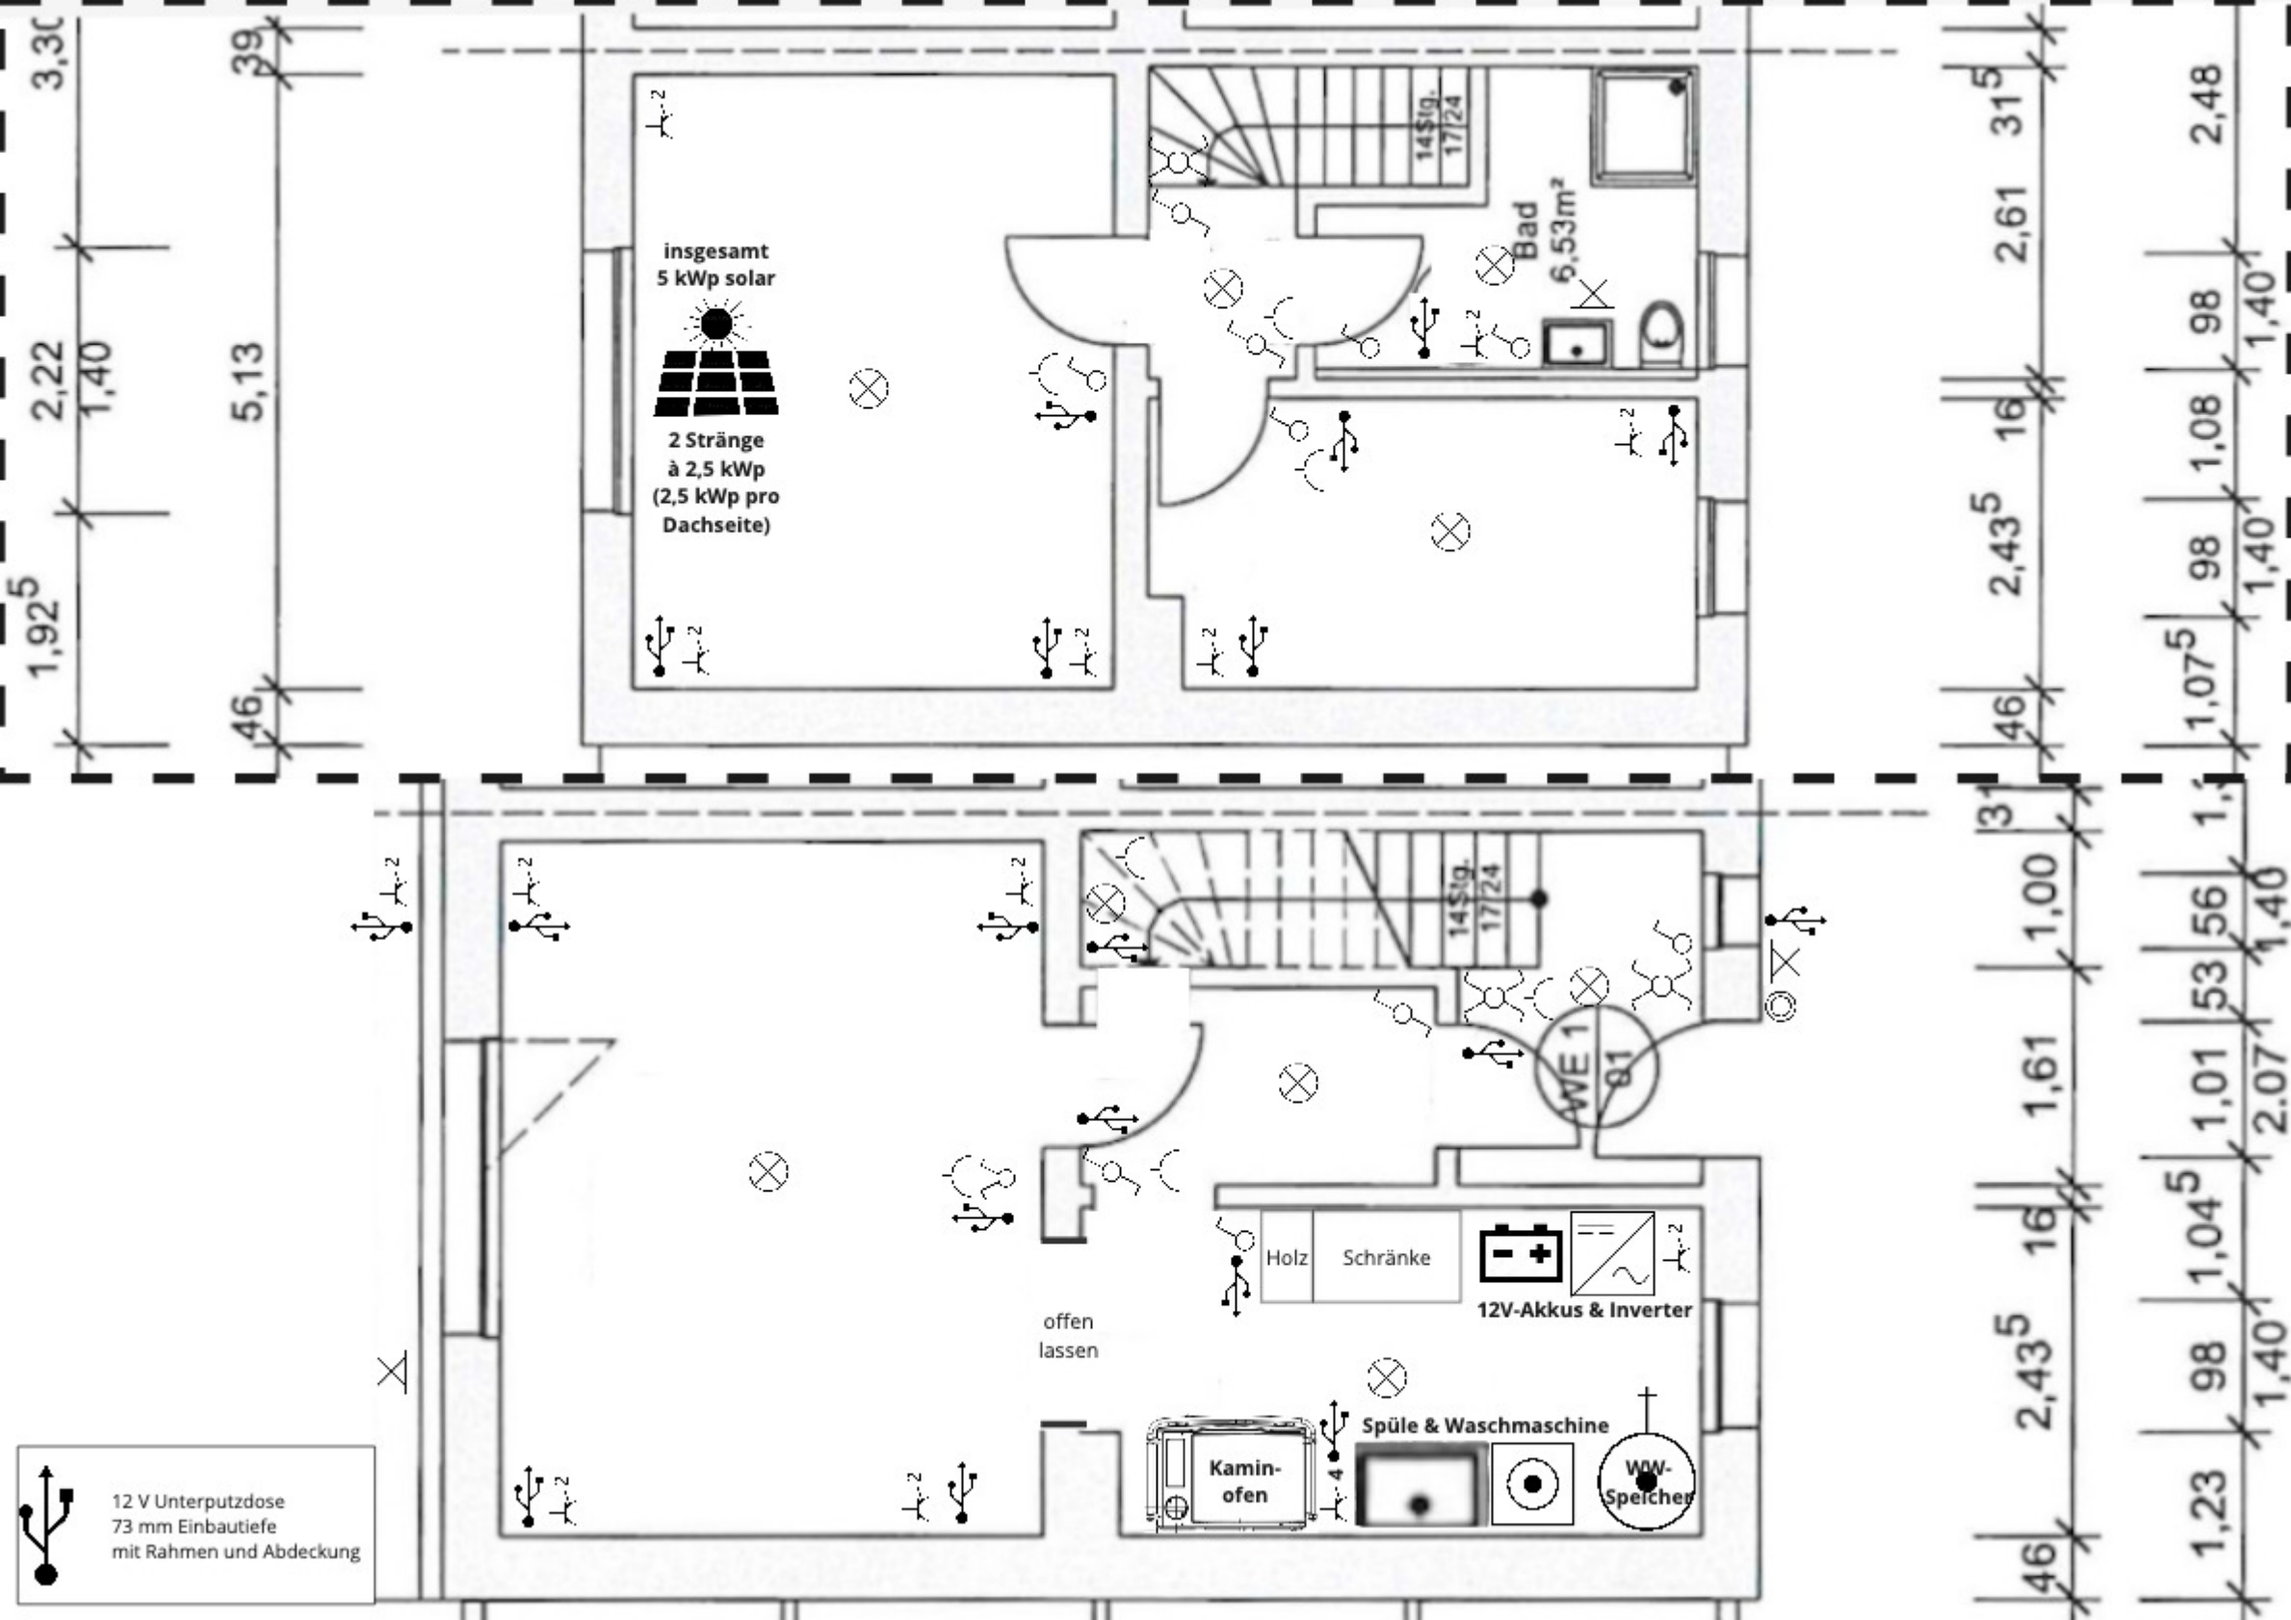

Stomanbieter / Hausanschluss
Zählerschrank
Zähler / SLS Smartmeter wenn E.DIS eHZ erlaubt
6A FILS Charger
Netzumschalter 3 Phasen + N
LS Unterverteiler
Küche - Kochen
3 phasen Herdanschluss (Last 400V) Wird in unserem Setup nicht benutzt, da zu hohe last
Küche Arbeitssteckdosen für Induktionsherdplatte(1500w), Termomix, Mini Backofen (2500w), Trockner (300W), Waschmaschine (2000W)
Wasserspeicher-Heizpatrone max 2000W
Abfrage aktueller Strompreise (15min-Takt)
Zuleitung Zählerschrank
Küche - Technik
Digitale Steuereinheit
Inverter & Charger
48V Verteiler & Absicherung
Akkubank 32KW/h
Jedes Zimmer
230V Steckdosen
Stromkeis Licht (inkl. Schalter)
48V Steckdosen (USB-C) 73 mm Einbautiefe
andere Geräte wie Überwachung, Starlink, Router,,.,.


insgesamt
5 kWp solar
2 Stränge
à 2,5 kWp
(2,5 kWp pro
Dachseite)
14 Stg.
17/24
Bad
6,53m²
WE 1
81
Holz
Schränke
12V-Akkus & Inverter
offen
lassen
Kamin-
ofen
Spüle & Waschmaschine
WW-
Speicher
12 V Unterputzdose
73 mm Einbautiefe
mit Rahmen und Abdeckung